



PLANTA - RUA DAS PEDRAS  
(ASFALTO DANIFICADO)

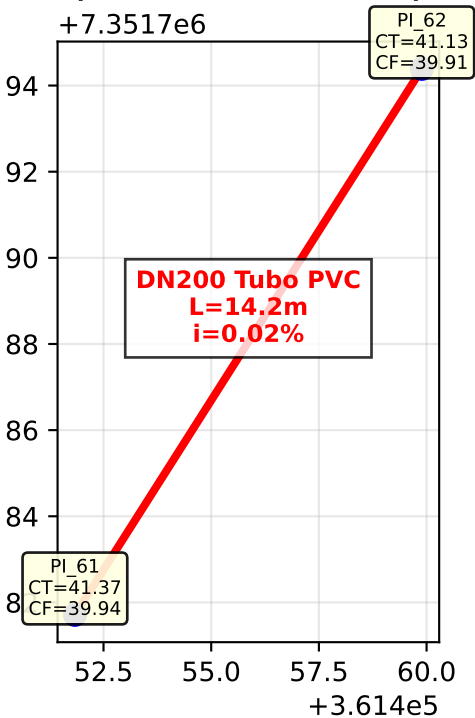

RESUMO DE MATERIAIS

| Material                 | Un    | Qtd  |
|--------------------------|-------|------|
| Tubo PVC DN200mm         | barra | 3    |
| Luva correr PVC DN200mm  | pç    | 2    |
| Anel borracha DN200mm    | pç    | 4    |
| Pasta lubrificante       | kg    | 0.12 |
| Areia lastro             | m³    | 1.14 |
| Areia envoltória         | m³    | 3.42 |
| Brita dreno              | m³    | 2.28 |
| PV concreto DN1200       | pç    | 1    |
| Ramal esgoto DN100       | pç    | 1    |
| Caixa inspeção           | pç    | 1    |
| Junção Y PVC DN200x100mm | pç    | 1    |
| PV Montante: PI_61       |       |      |
| PV Jusante: PI_62        |       |      |

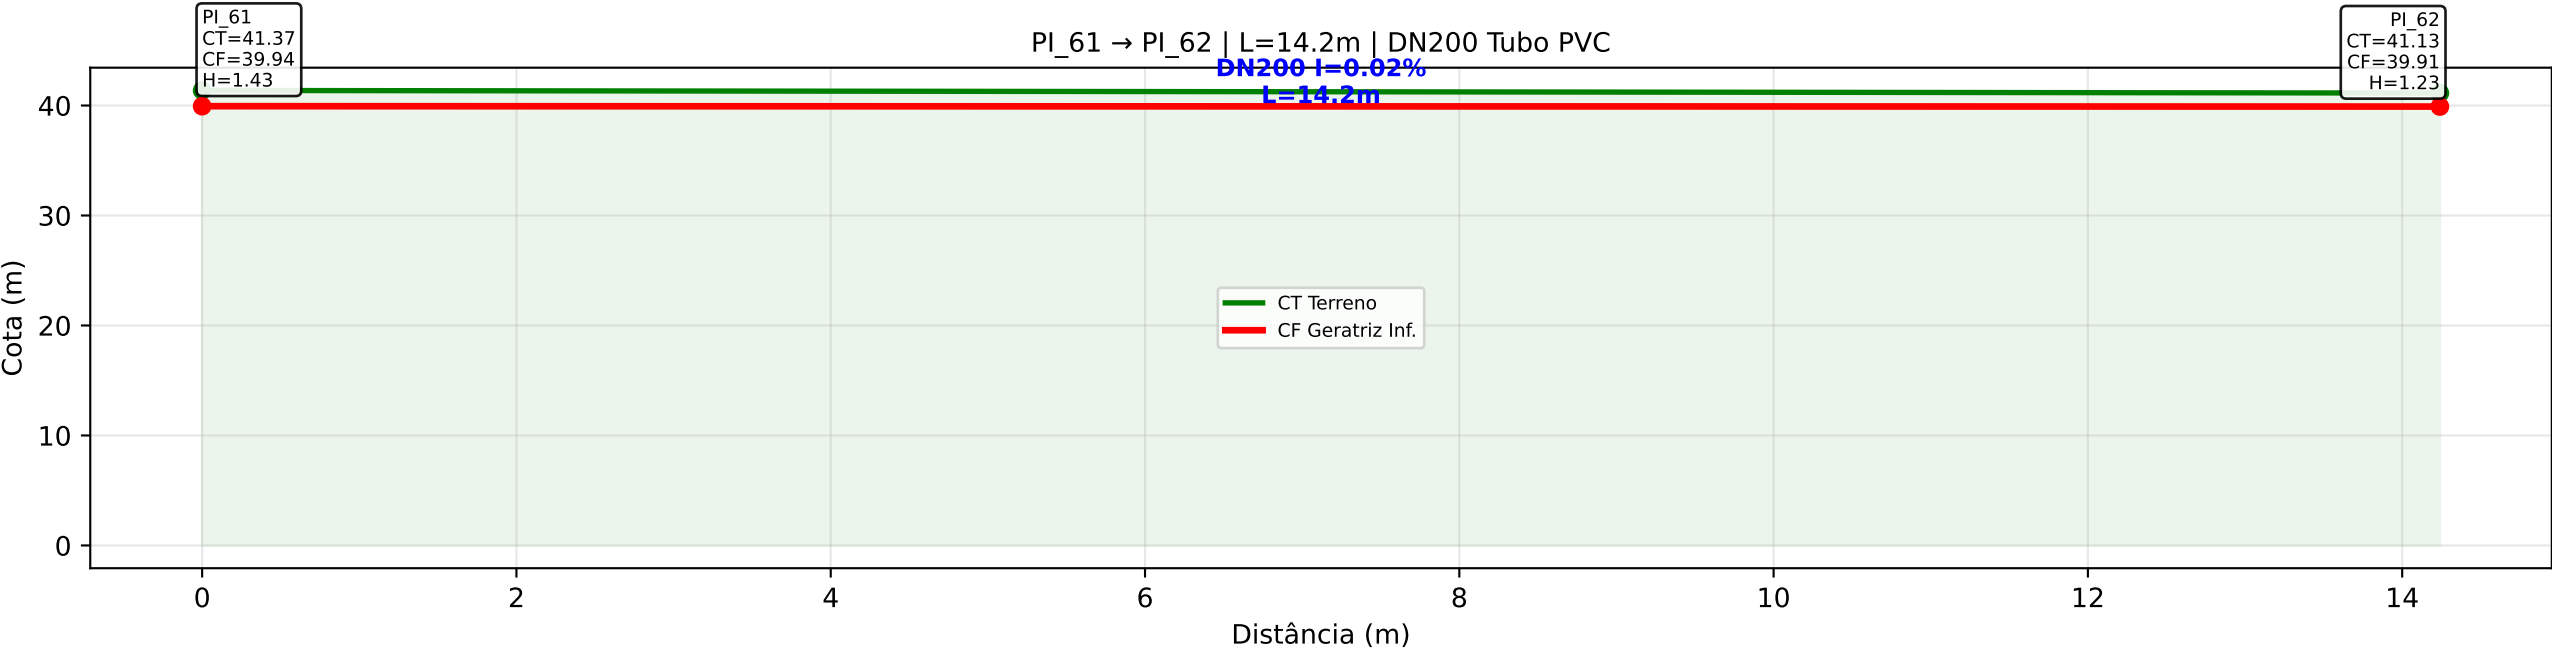

| Estaca | CT(m)  | CF(m)  | Prof(m) | Dist(m) | DN/Mat        | Decl(%) |
|--------|--------|--------|---------|---------|---------------|---------|
| PI_61  | 41.371 | 39.939 | 1.432   |         |               |         |
| PI_62  | 41.132 | 39.905 | 1.227   | 14.24   | DN200 Tubo PV | 0.02%   |

NS005

Rua: RUA DAS PEDRAS  
(ASFALTO DANIFICADO)  
PI 61 ao PI 62  
DN200 Tubo PVC | 14.2m  
Decl: 0.018%  
V=4.45m/s | Tau=89.1Pa

Custo: R\$ 12,958.40

SE LIGA NA REDE  
23/03/2026